

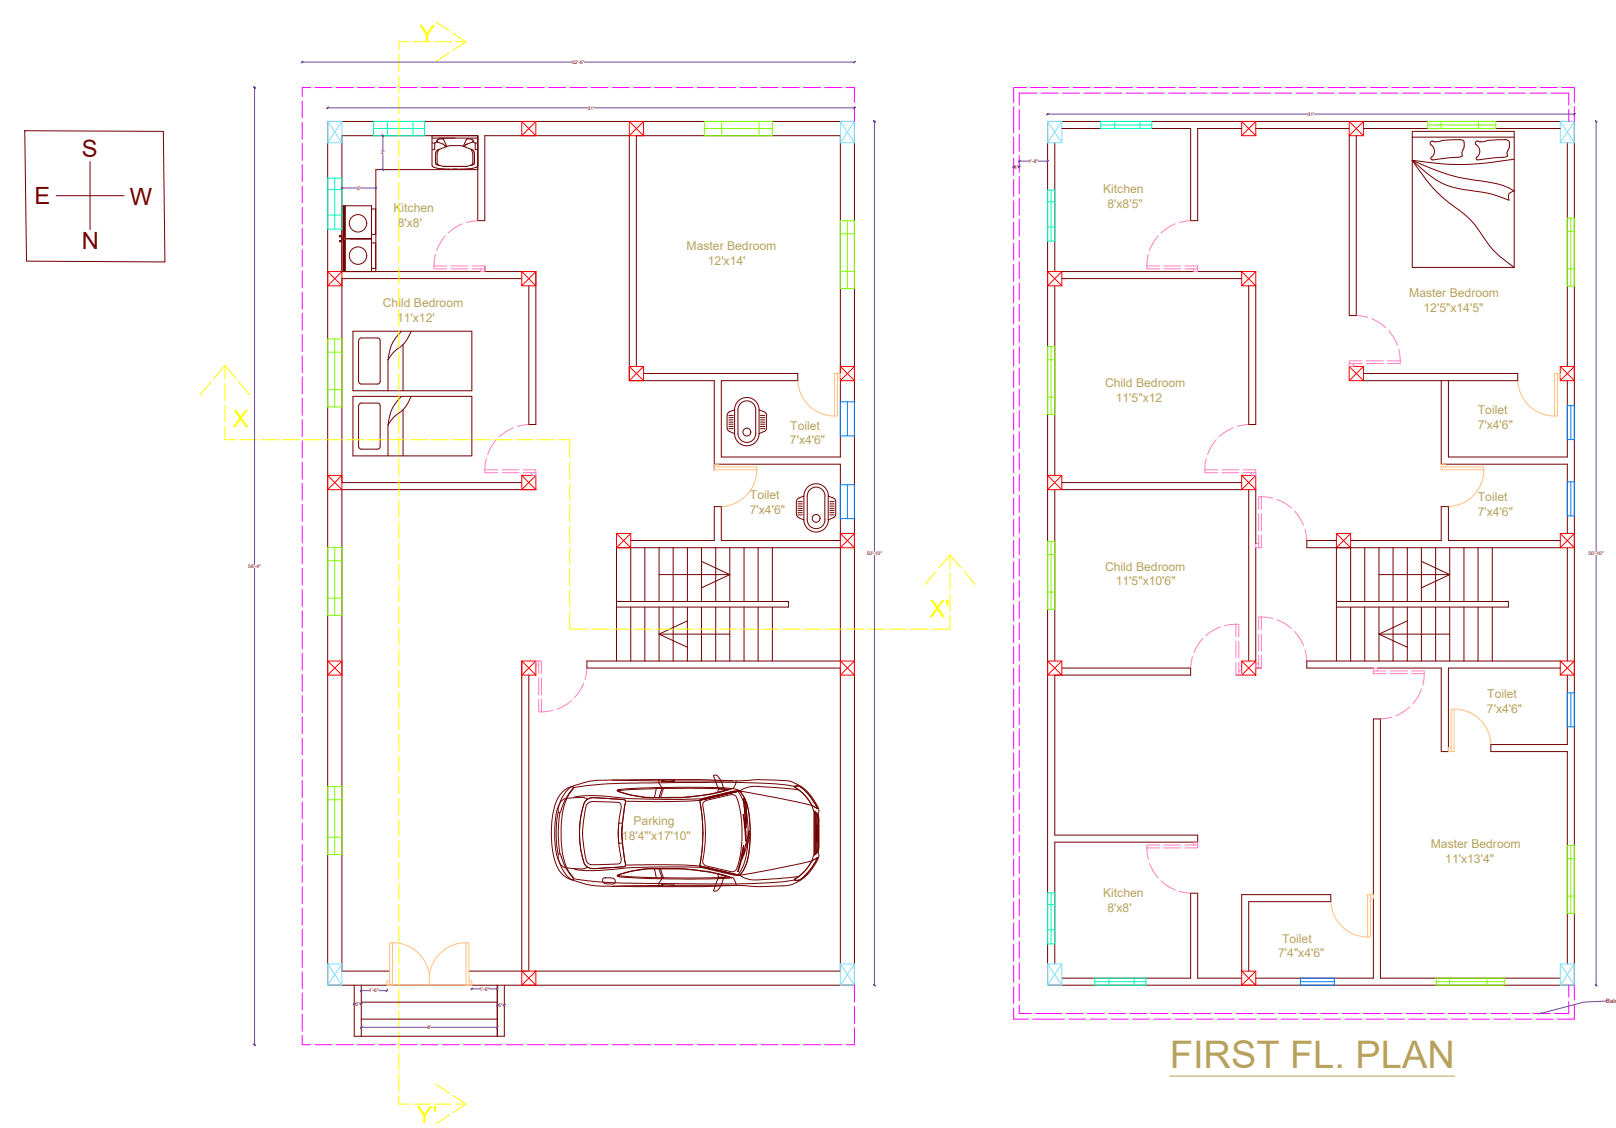



Main Door [D] = 5'x7'
Door [D1] = 3'x7'
Door [D2] = 2'6"x7'
Window [W] = 4'x4'
Window [W2] = 3'x4'
Ventilation [V] = 2'x1'6"

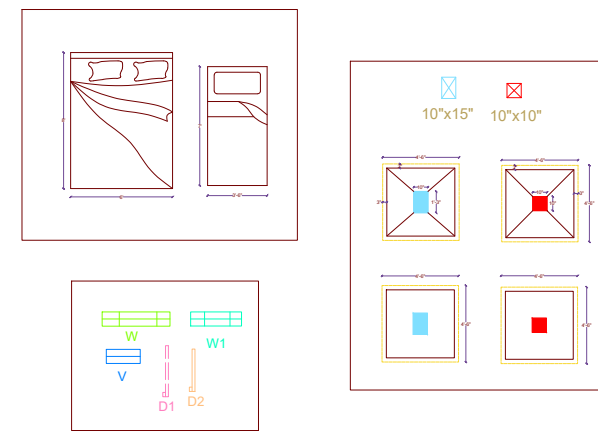


FIRST FL. PLAN

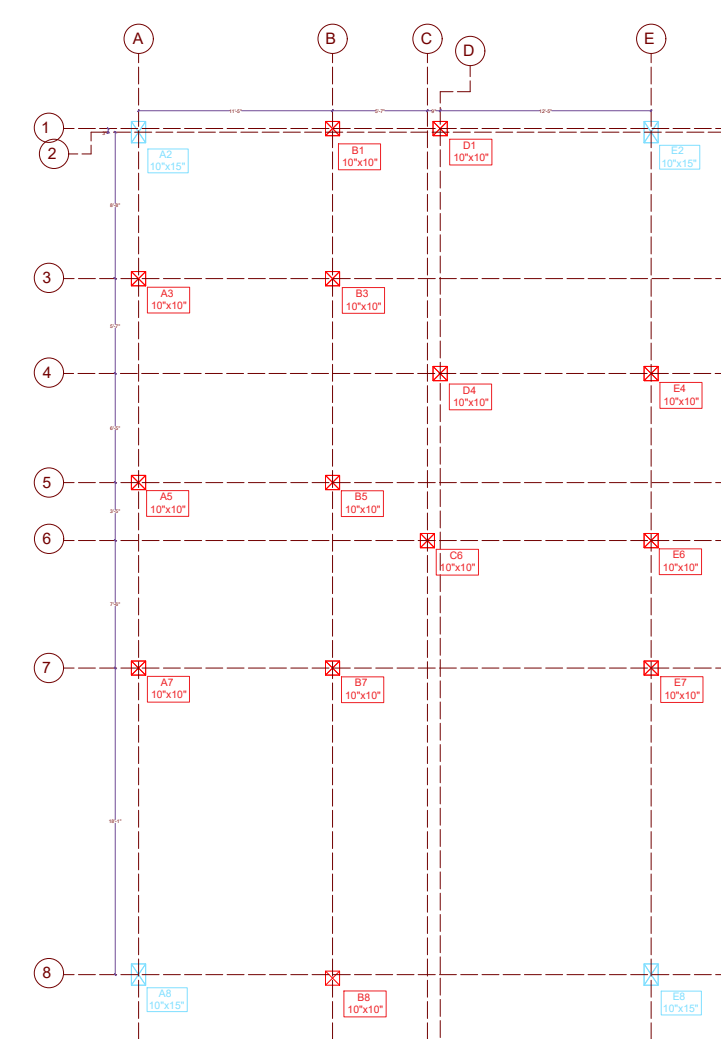


COLUMN LAYOUT

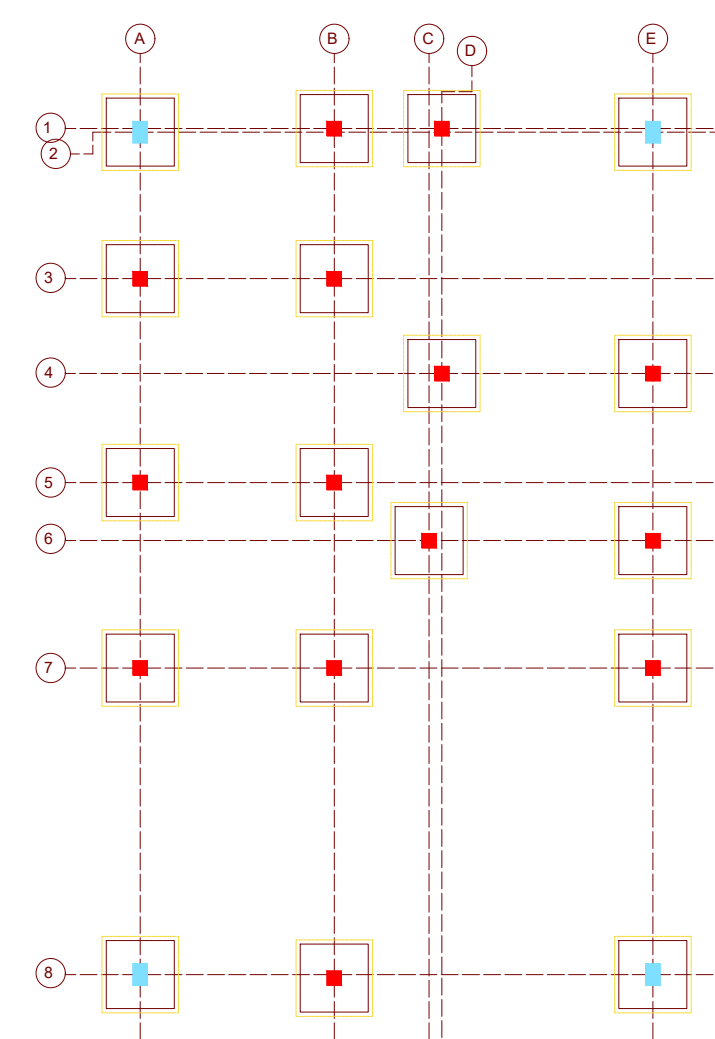

FOOTING LAYOUT WITHOUT SLAB

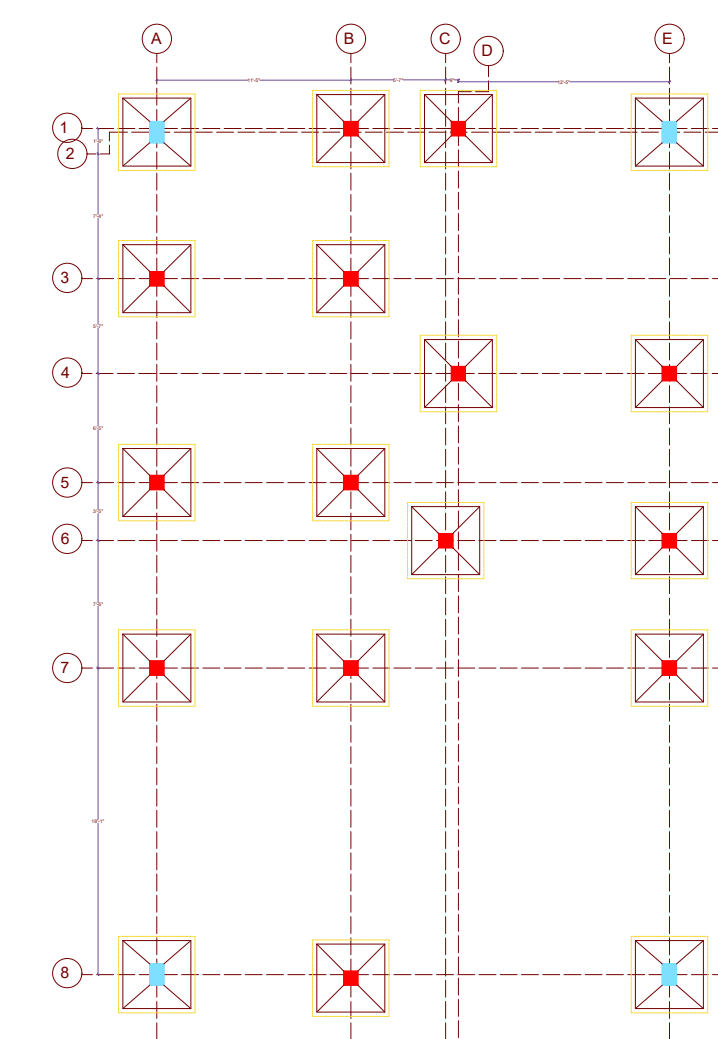


FOOTING LAYOUT WITH SLAB

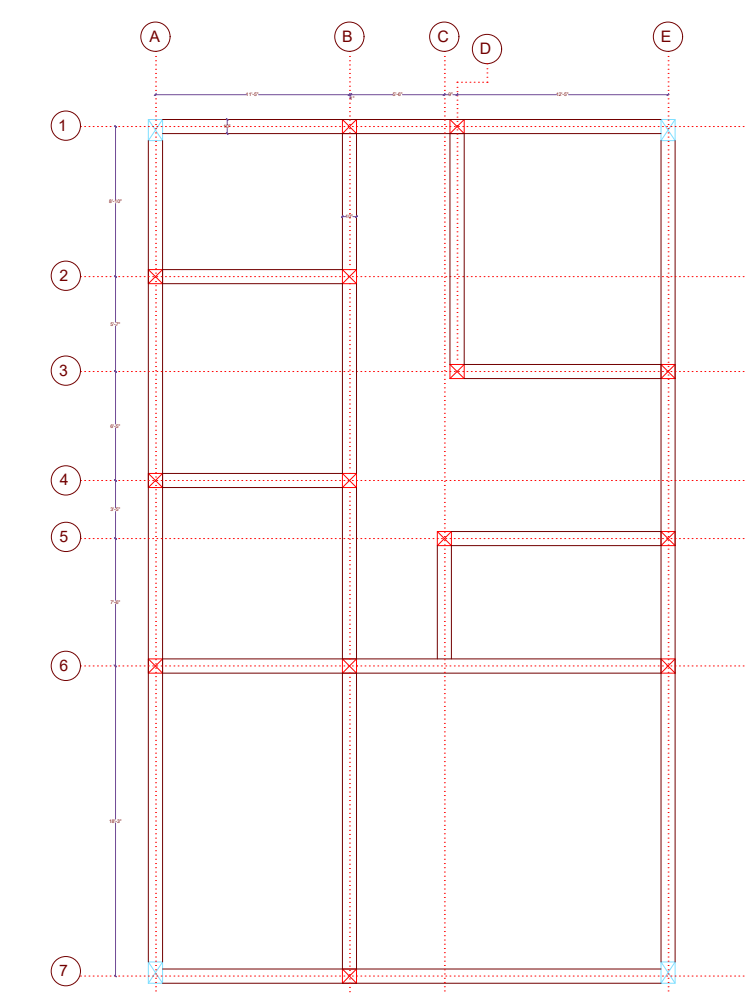


BEAM LAYOUT OF GROUND FL.




GROUND FL. PLAN

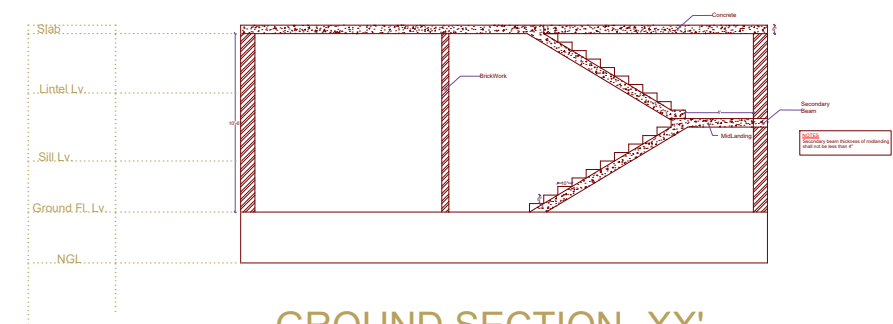

GROUND SECTION- XX'

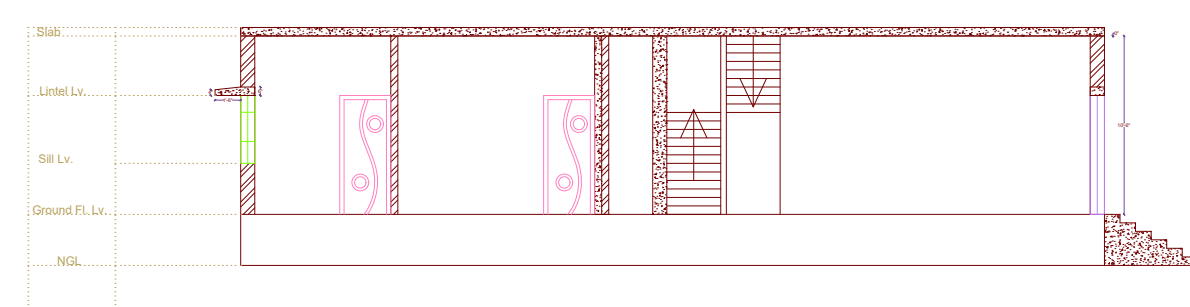

GROUND SECTION- YY'

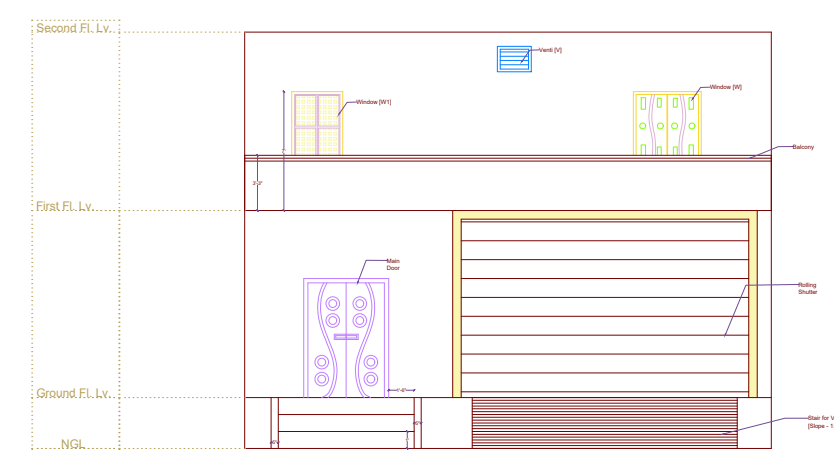

FRONT SIDE ELEVATION