




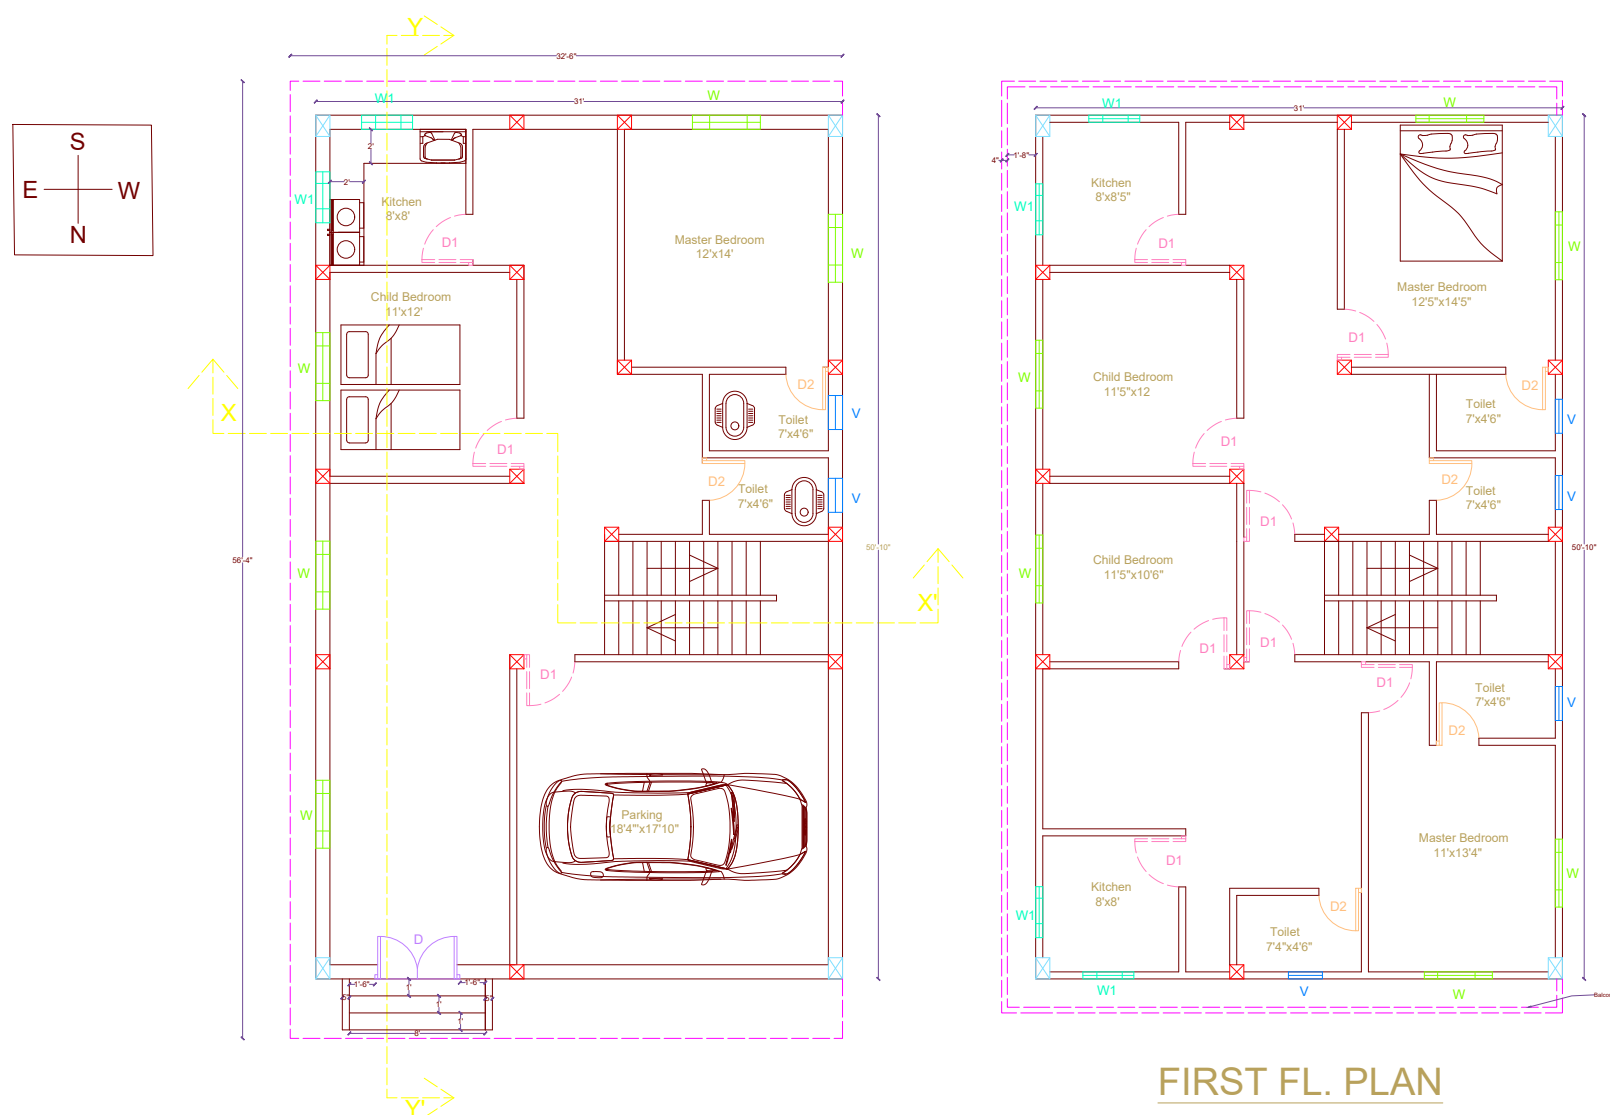


FIRST FL. PLAN

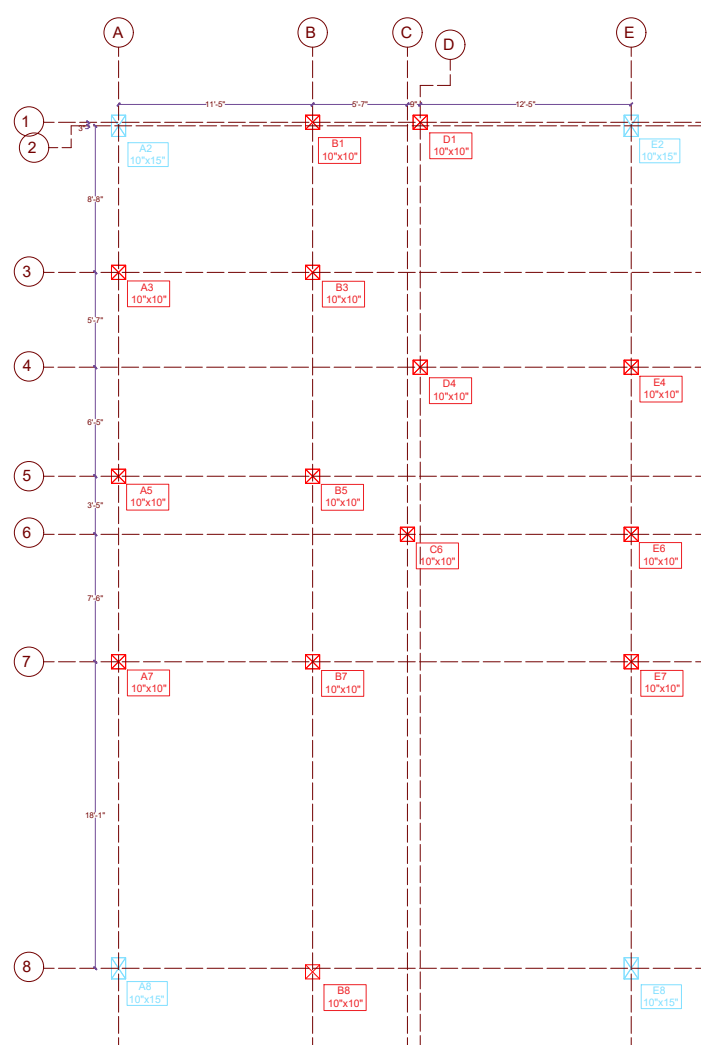


COLUMN LAYOUT

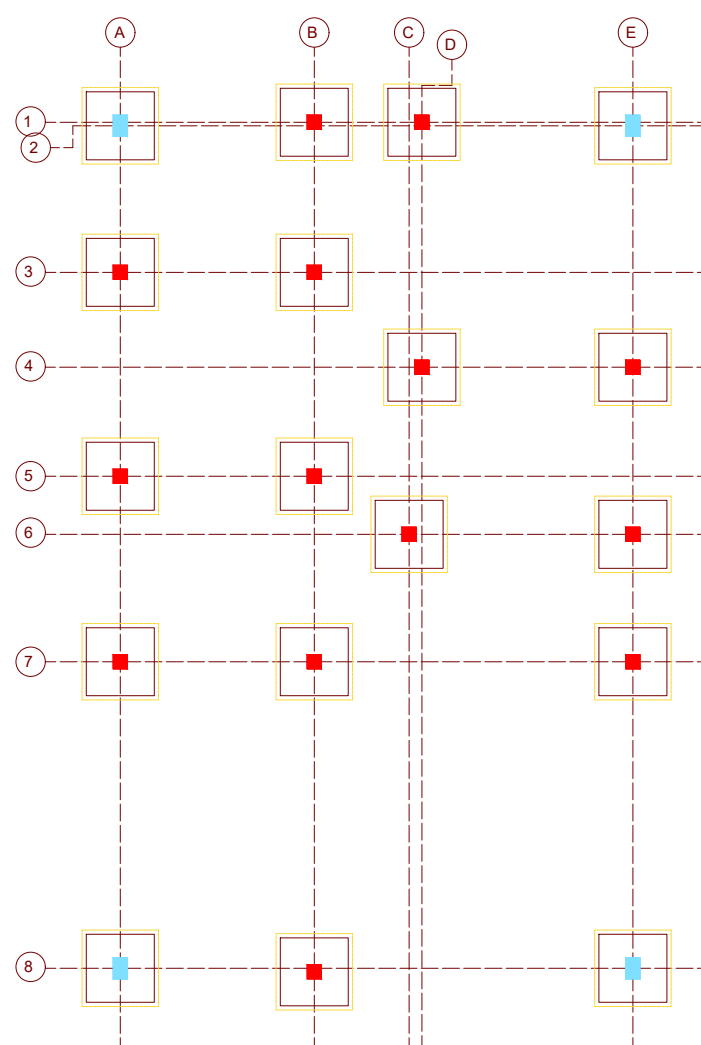

FOOTING LAYOUT WITHOUT SLAB

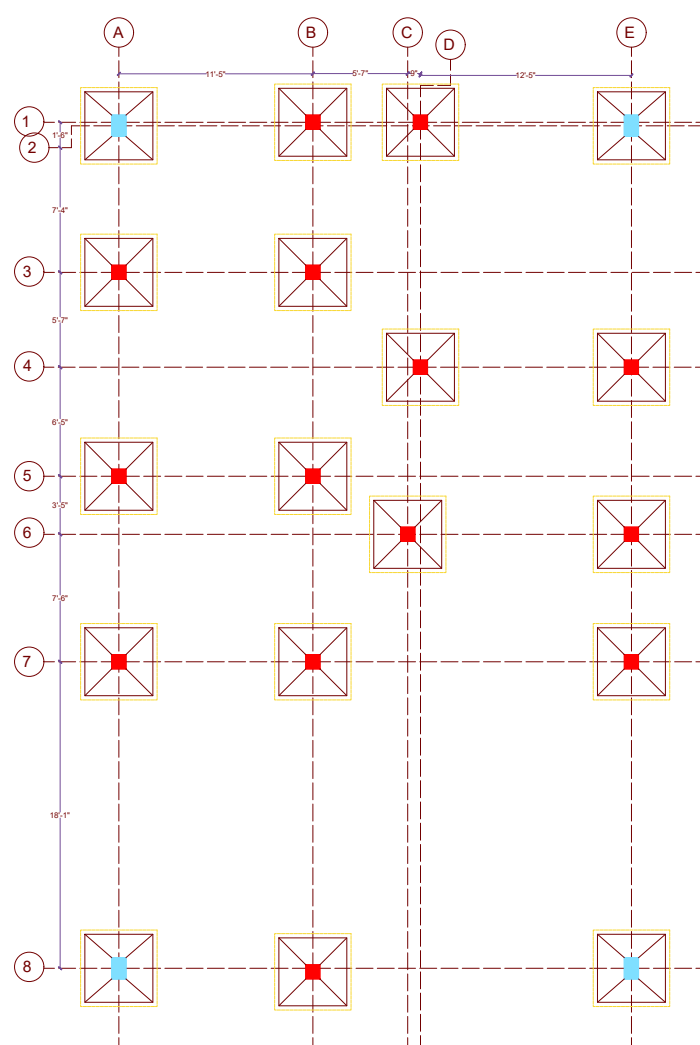


FOOTING LAYOUT WITH SLAB

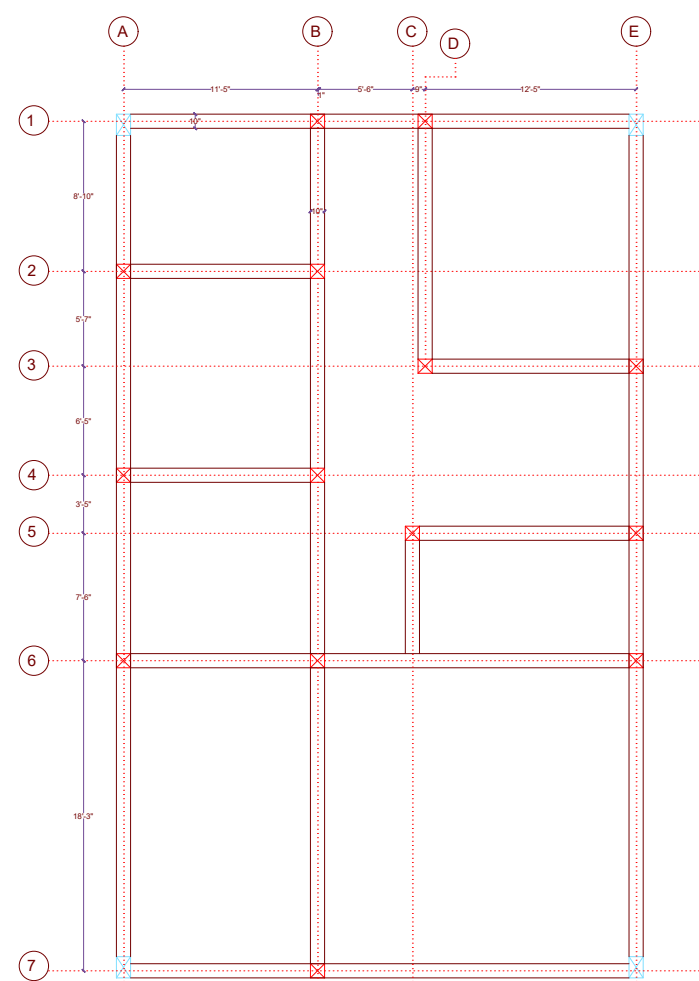


BEAM LAYOUT OF GROUND FL.




GROUND FL. PLAN

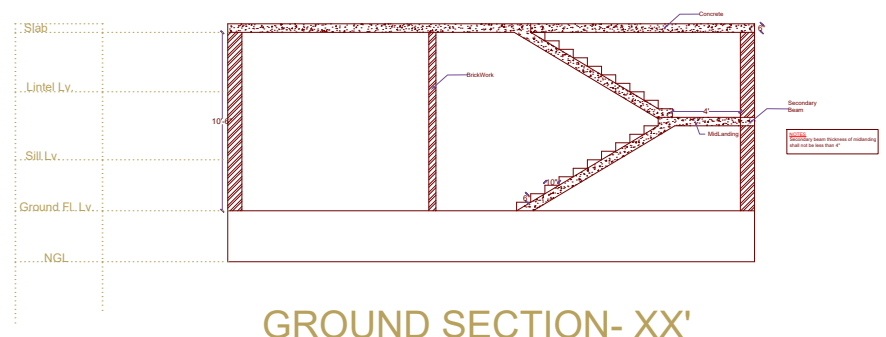

GROUND SECTION- XX'

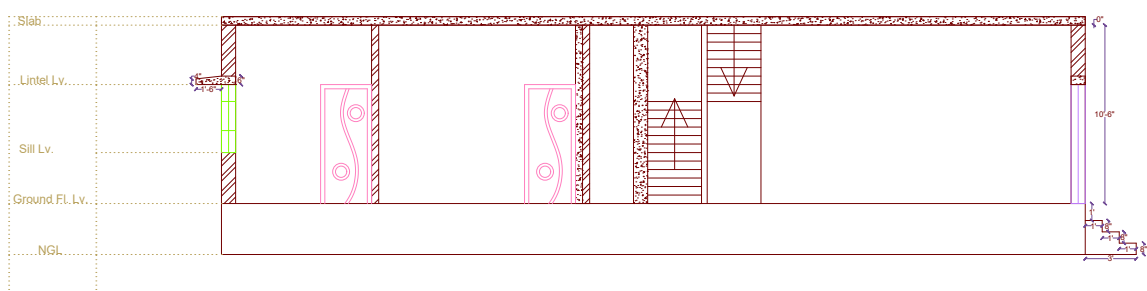

GROUND SECTION- YY'

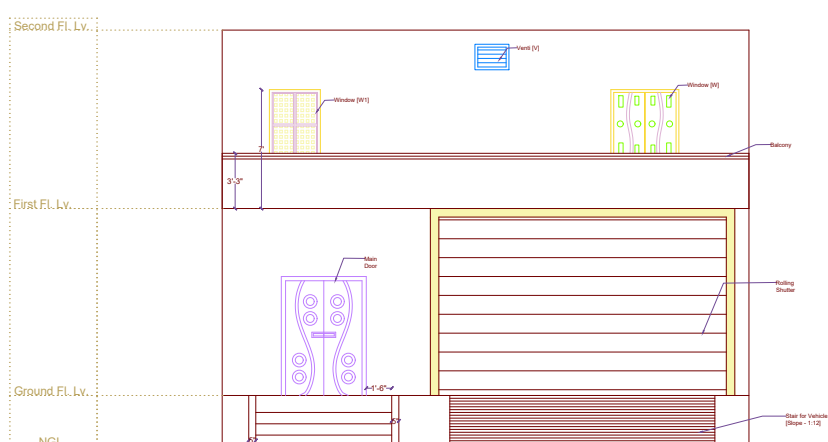

FRONT SIDE ELEVATION

SCHEDULE OF WINDOW AND DOOR

Main Door [D] = 5'x7'

Door [D1] = 3'x7'

Door [D2] = 2'6"x7'

Window [W] = 4'x4'

Window [W2] = 3'x4'

Ventilation [V] = 2'x1'6"

Ground Floor

Exterior Wall = 10"

Interior Wall = 5"

First Floor

All Wall = 5"

